
CORPORATE DESIGN

AC Studio

- This is a group project in 2023 winter.
- I was responsible for logo design, material selection, design and drawing of floor plan and elevations, modeling and rendering.
- The idea behind this design was to create a comfortable working environment with a natural style.
- The design attempts to separate quiet areas from noisy ones.

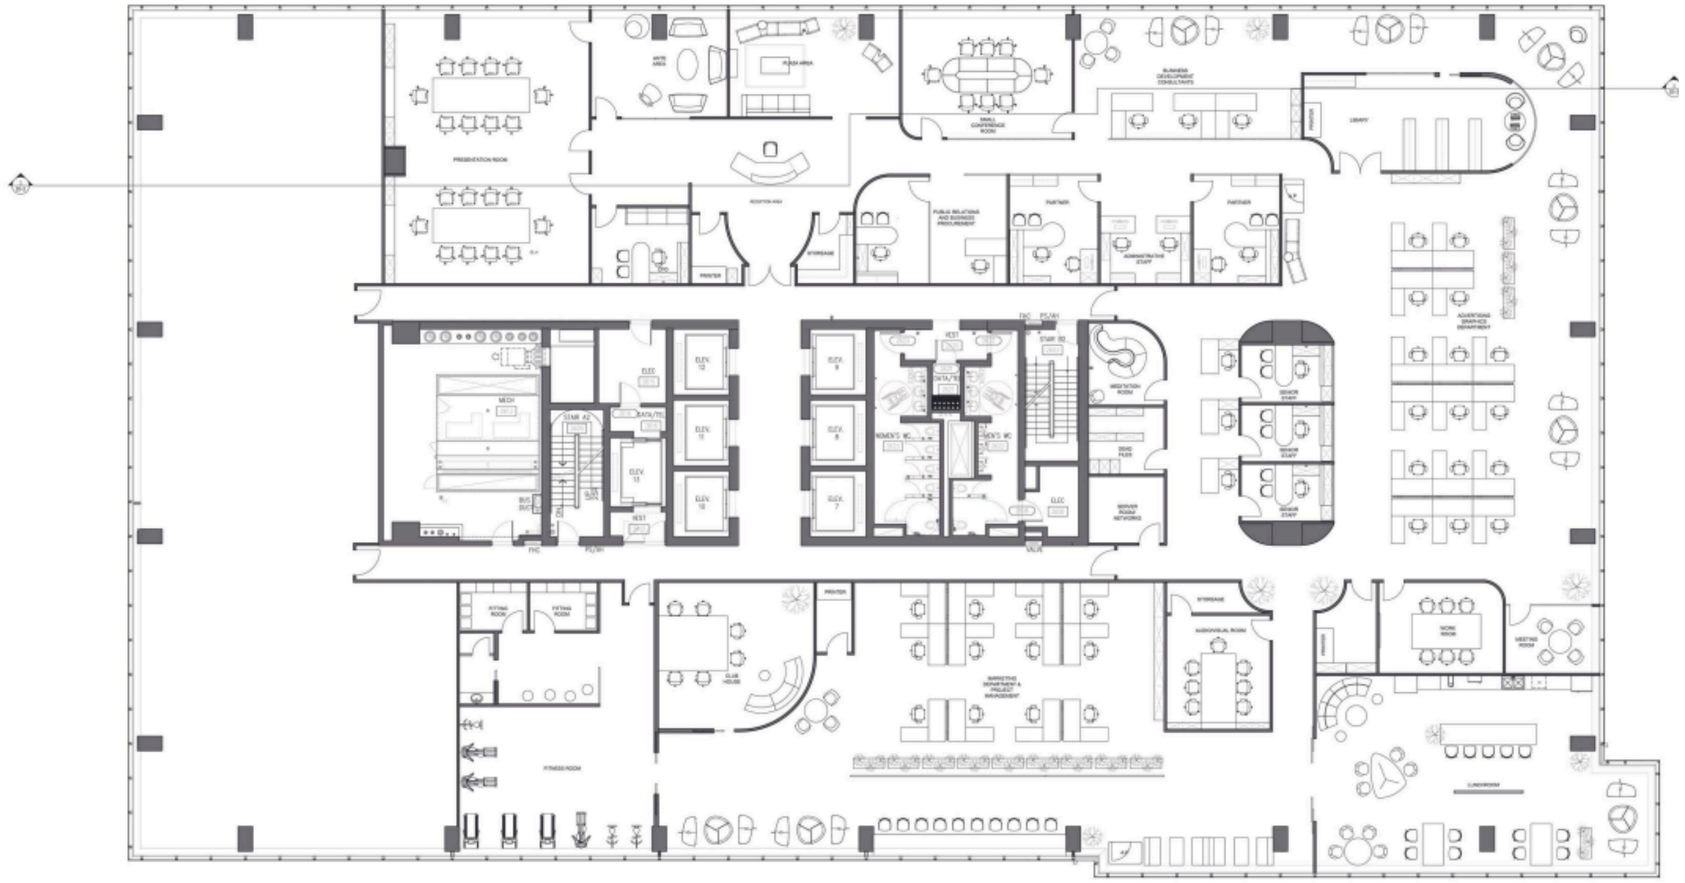

AC STUDIO

RENDERED FLOOR PLAN

Carpet Tile



Carpet Tile



Marble Flooring



Carpet Tile



Wood Flooring








Reception Area Perspective

REFLECTED CEILING PLAN

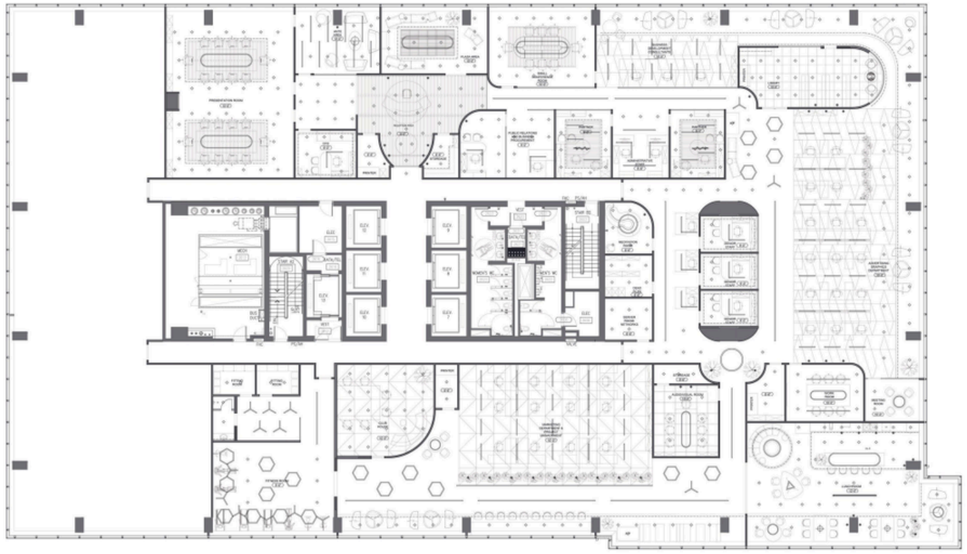












Lunchroom Perspective



Plaza Area Perspective

RENDERED ELEVATIONS

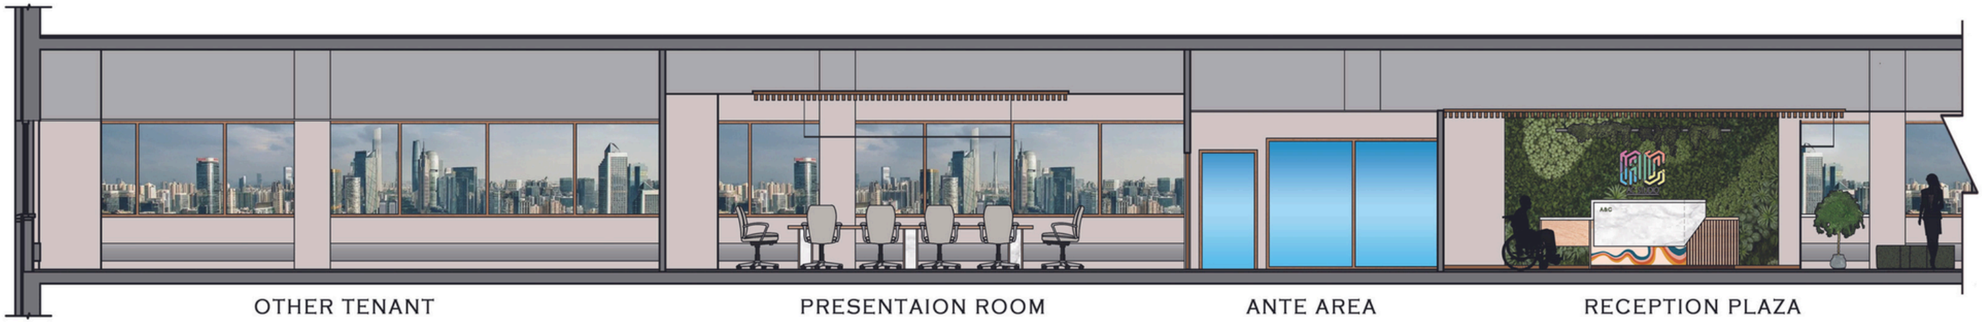






SAMPLE BOARD







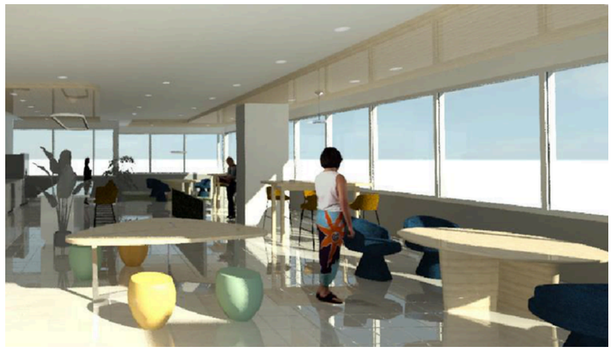







PROCESS WORKS