
ACOUSTIC WALL

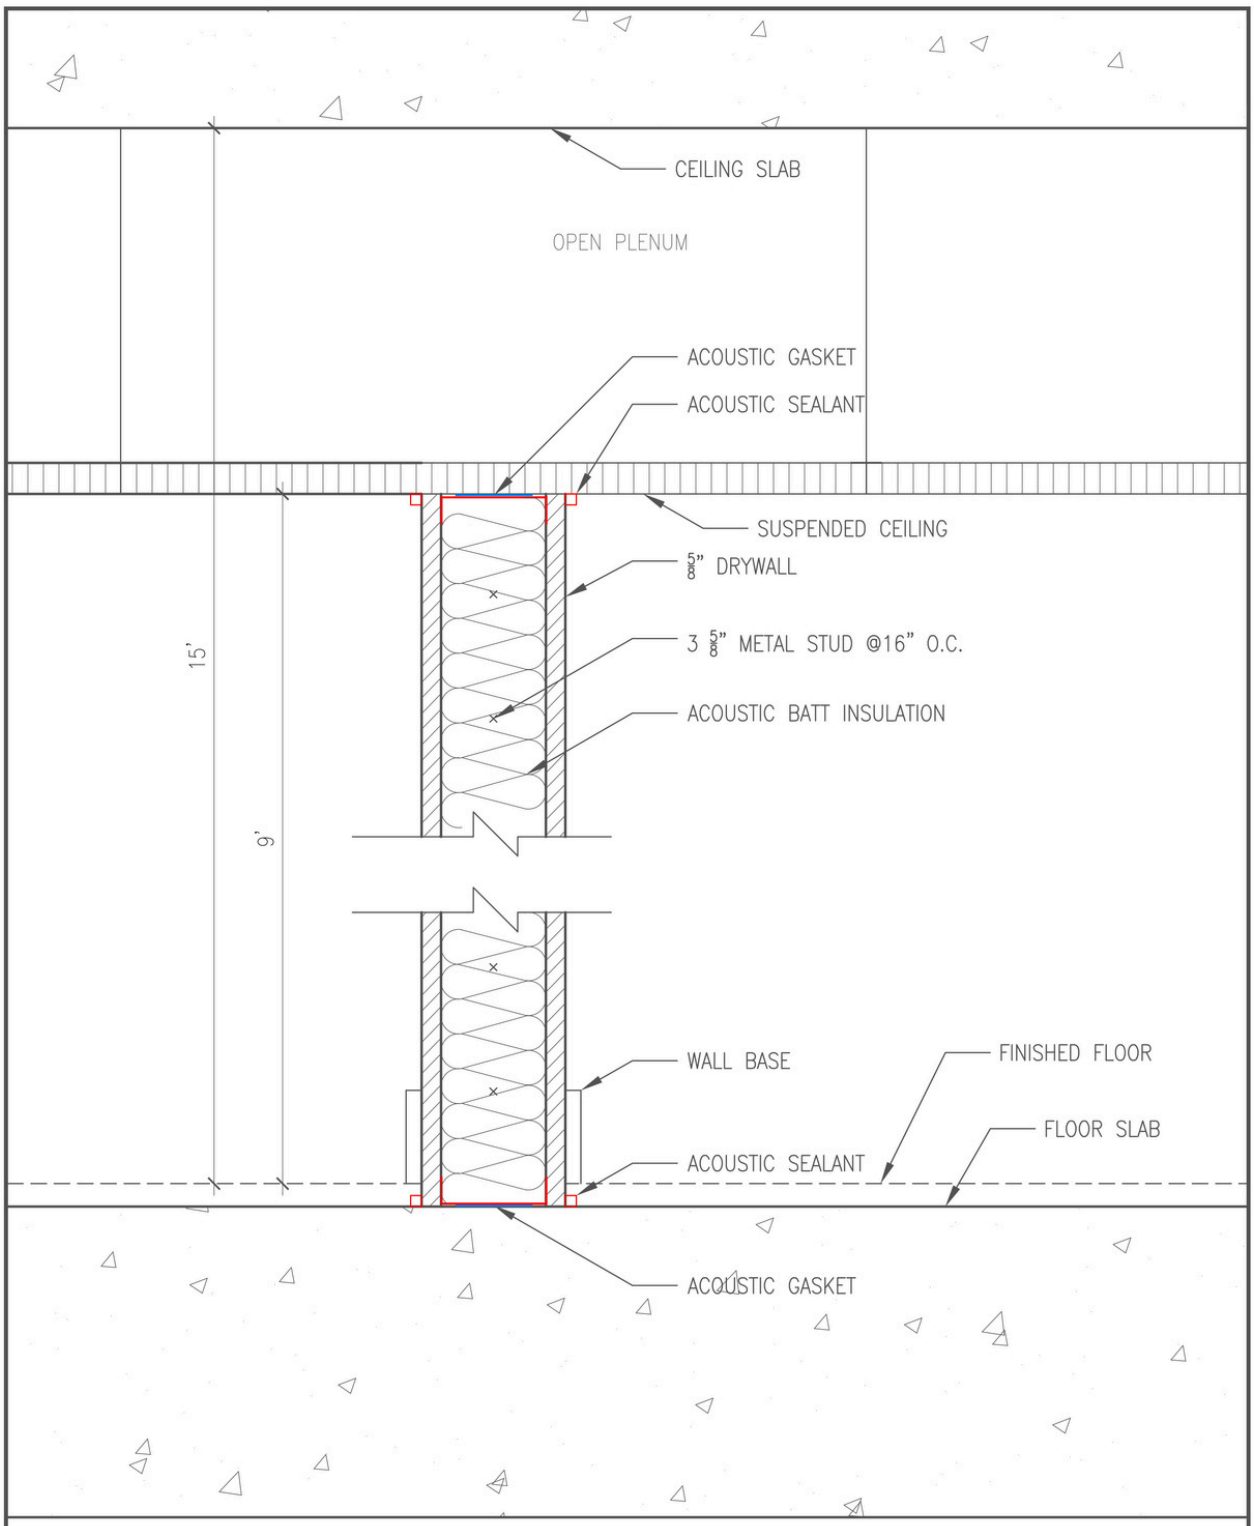

1 / ID-1 ACOUSTIC PARTITION STC 35-40

3"=1'-0"


NOTE:

Sheridan | Get Creative
INSTITUTE OF TECHNOLOGY & ADVANCED LEARNING
BACHELOR of INTERIOR DESIGN

DRAWING:	ACOUSTIC WALL
PROJECT:	WALL SECTIONS
DATE:	280324
SCALE:	3"=1'-0"
NAME:	Q.TAO
CHECKED:	N.MOHMOUD

ID-1

FIRE-RATED WALL

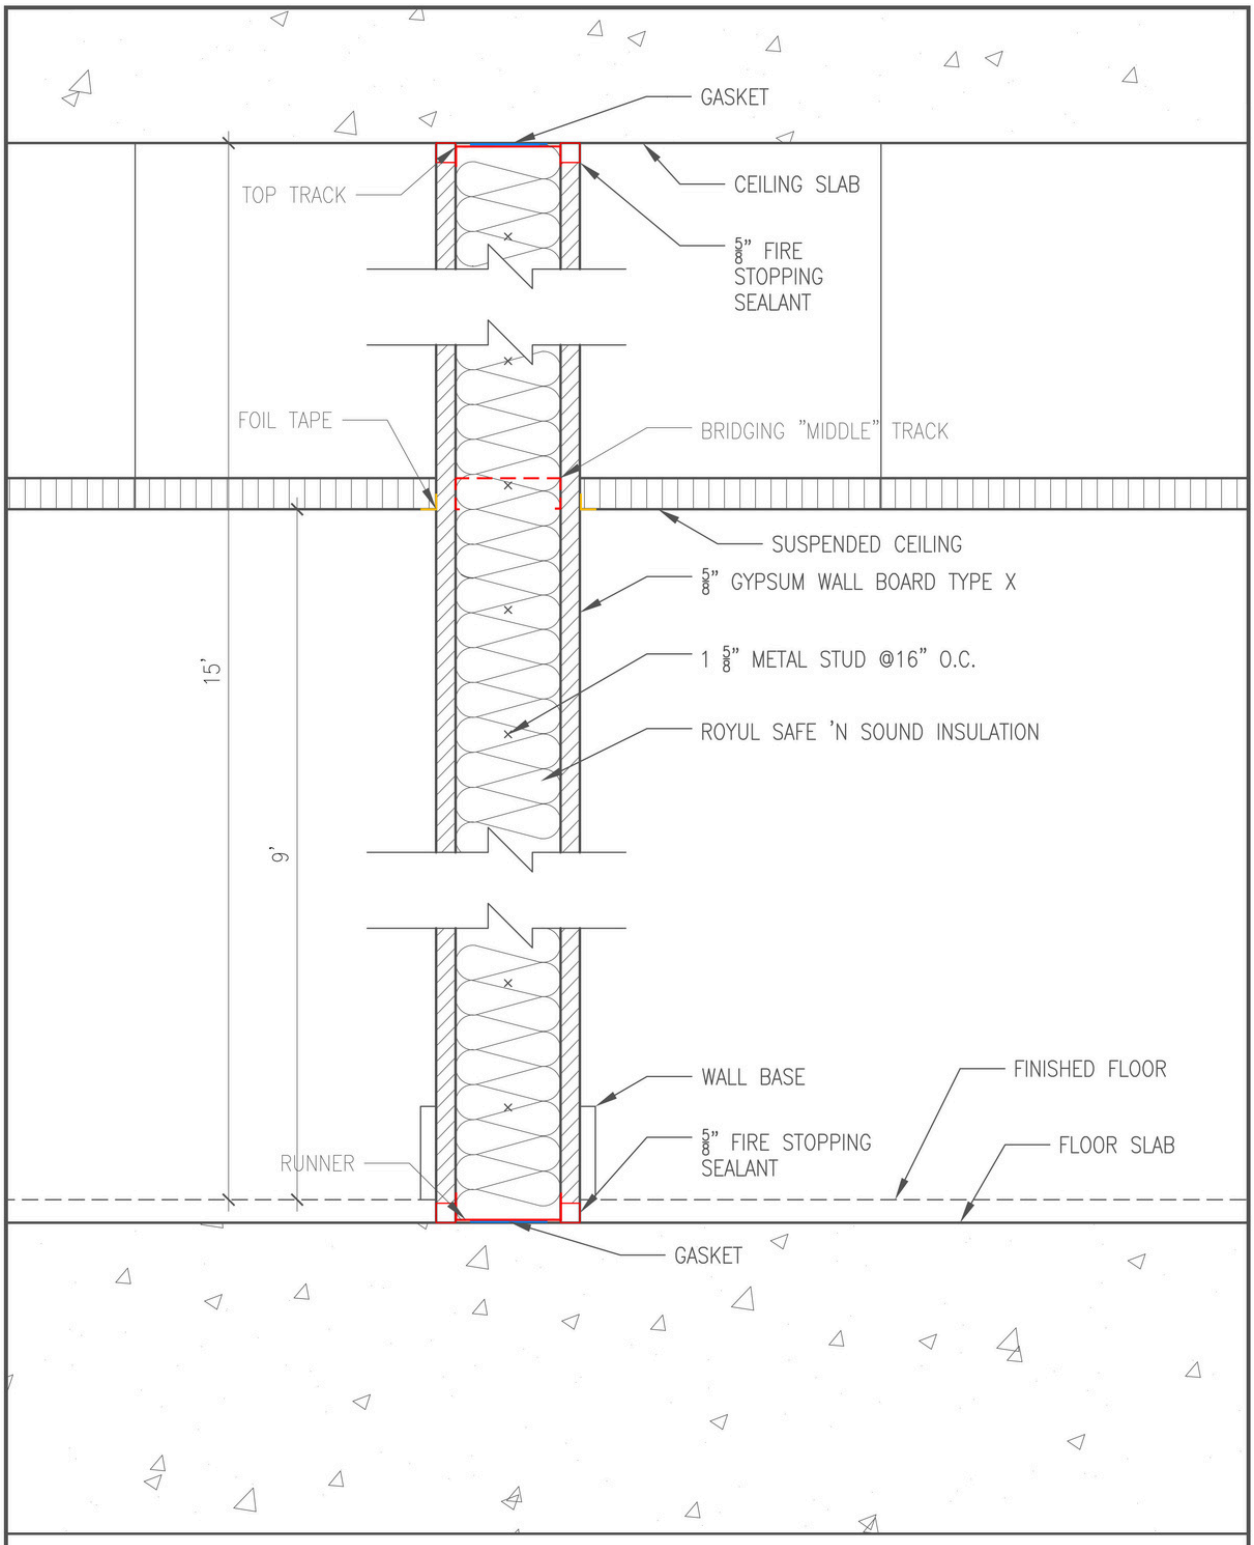

1 / ID-2 — 1 HR FIRE-RATED PARTITION

3"=1'-0"


NOTE:

Sheridan | Get Creative
INSTITUTE OF TECHNOLOGY & ADVANCED LEARNING
BACHELOR of INTERIOR DESIGN

DRAWING:	FIRE RATED WALL
PROJECT:	WALL SECTIONS
DATE:	280324
SCALE:	3"=1'-0"
NAME:	Q.TAO
CHECKED:	N.MOHMOUD

ID-2

MOISTURE CONTROL WALL

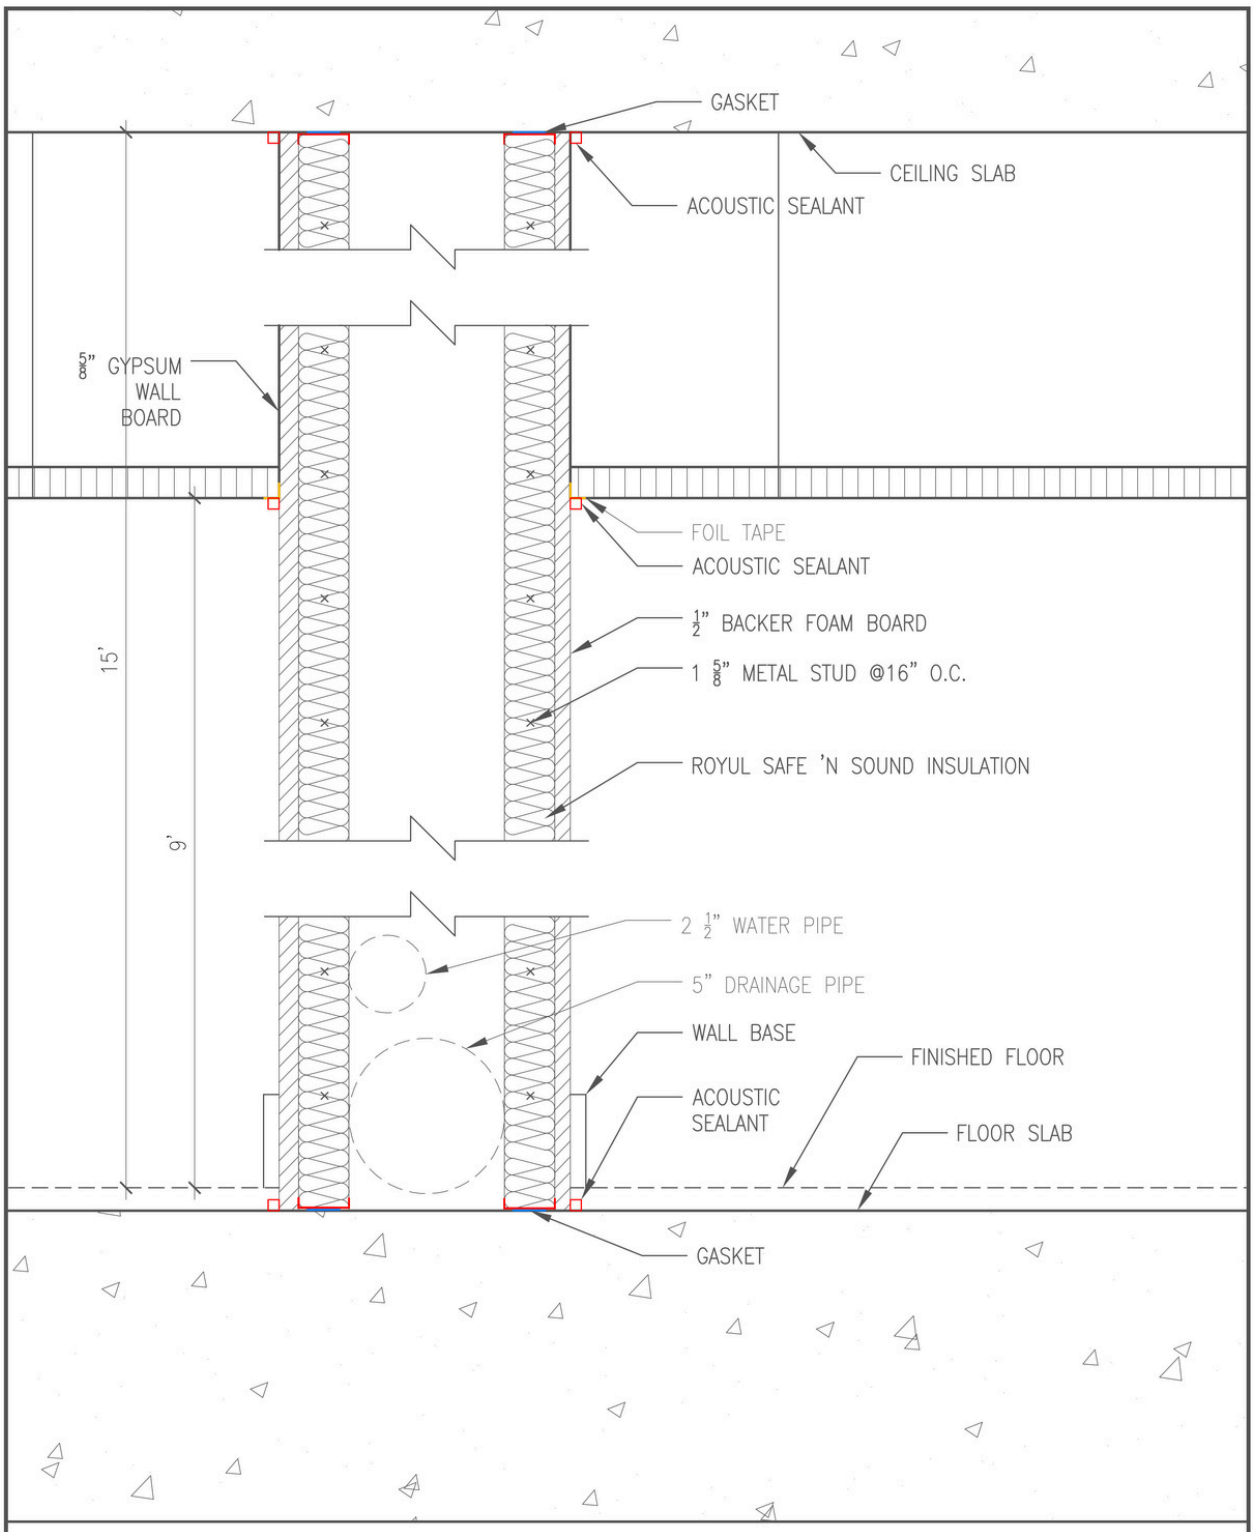

1 / ID-3 MOISTURE CONTROL PLUMBING CHASE WALL

3"=1'-0"


NOTE:

Sheridan | Get Creative
INSTITUTE OF TECHNOLOGY & ADVANCED LEARNING
BACHELOR of INTERIOR DESIGN

DRAWING:	PLUMBING WALL
PROJECT:	WALL SECTIONS
DATE:	280324
SCALE:	3"=1'-0"
NAME:	Q.TAO
CHECKED:	N.MOHMOUD


ID-3

WALL TYPES

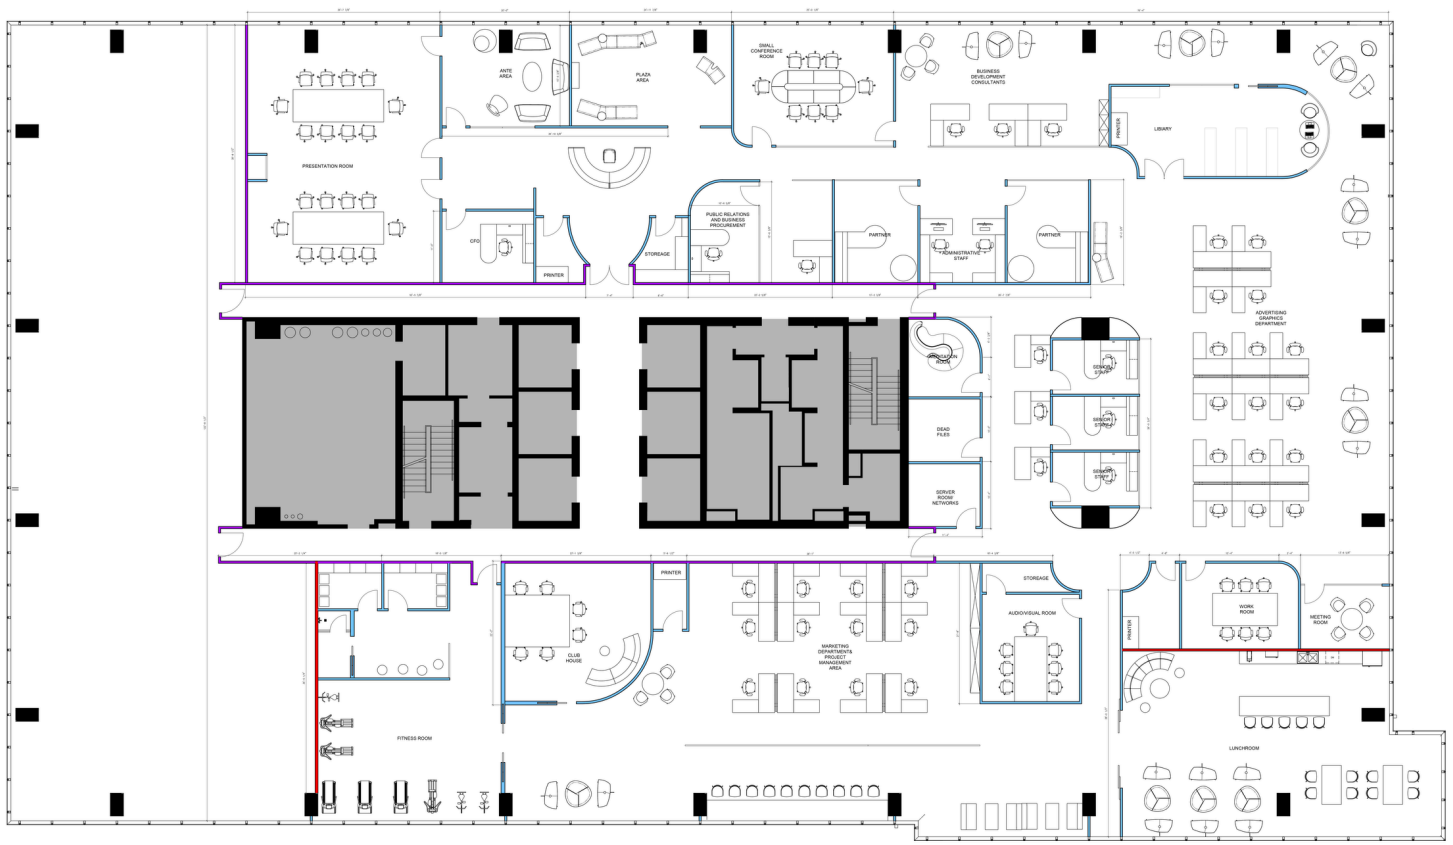


	WALL TYPE A	4-5/8" ACOUSTIC WALL WITH TYPE X G.W.B
	WALL TYPE B	4-5/8" 1 HR FIRE RATED WALL
	WALL TYPE C	6" PLUMBING WALL


SKETCHES

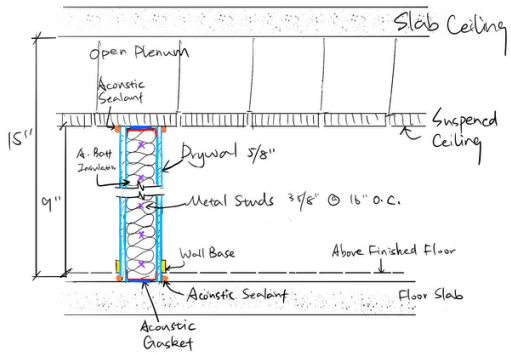


1 / JD-1 Acoustic partition w/s Suspened Ceiling NTC

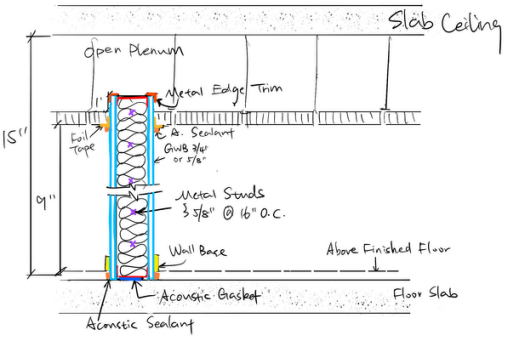


2 / JD-1 Acoustic Partition 12" Above NTS

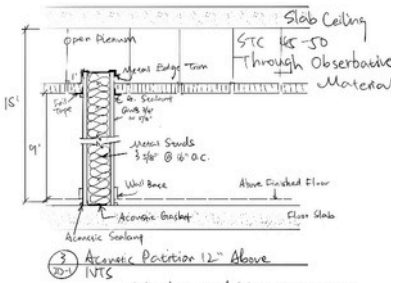


3 / JD-1 Acoustic Partition 12" Above NTS

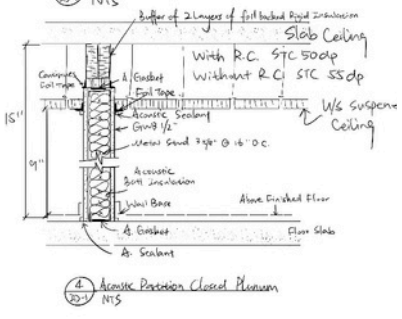


4 / JD-1 Acoustic Partition Closed Plenum NTS

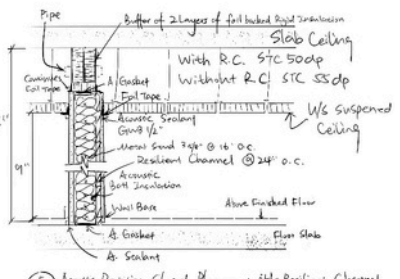


5 / JD-1 Acoustic Partition Closed Plenum with Resilient Channel NTS

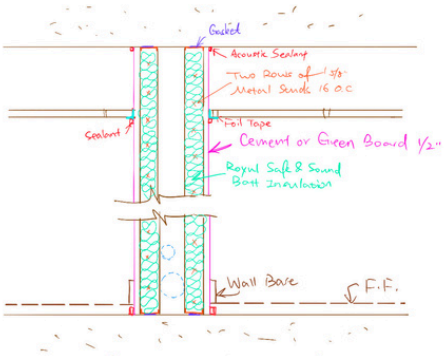


Plumbing Chase Wall Double Studs

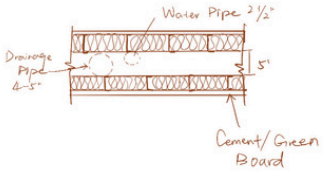

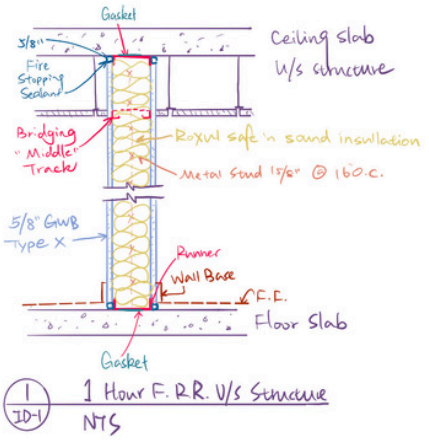


1 / JD-1 1 Hour F.R.R. U/s Structure NTS

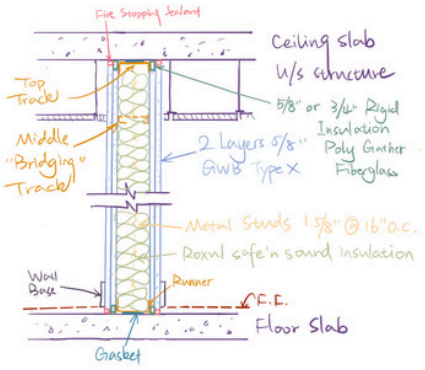


2 / JD-1 2 Hour F.R.R. U/s Structure NTS

(1)

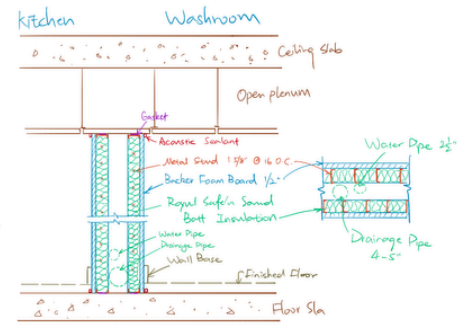

1 / JD-1 Double Stud Chase Wall NTS

(2)

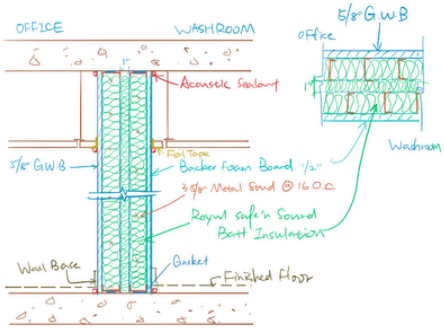

2 / JD-1 Chase Wall Between Office & Washroom NTS