

CORPORATE MILLWORK DESIGN




Front View

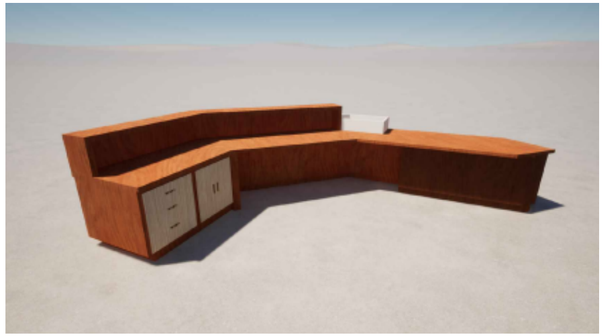

Back View

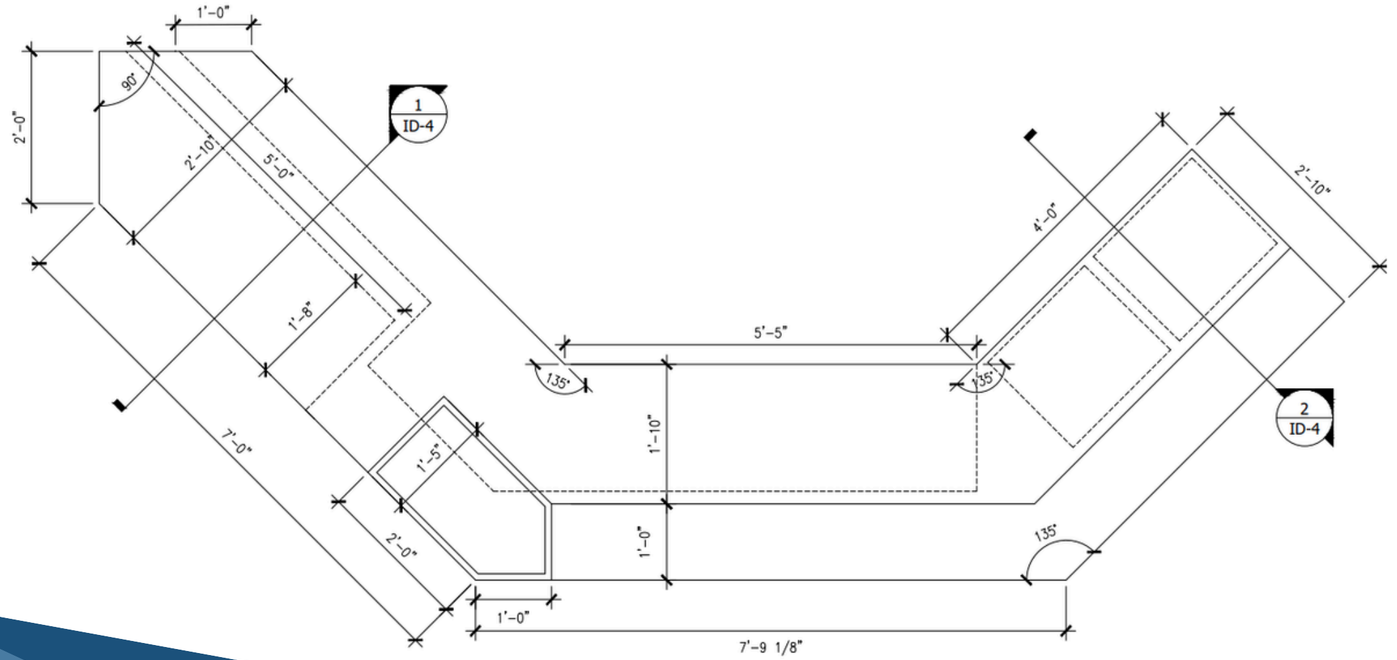


- This is an indivisual project in 2023 winter.
- I designed a reception desk based on the theme of nature.
- I used wood finishes, wood grills, and planters to make it blend into the plant wall.

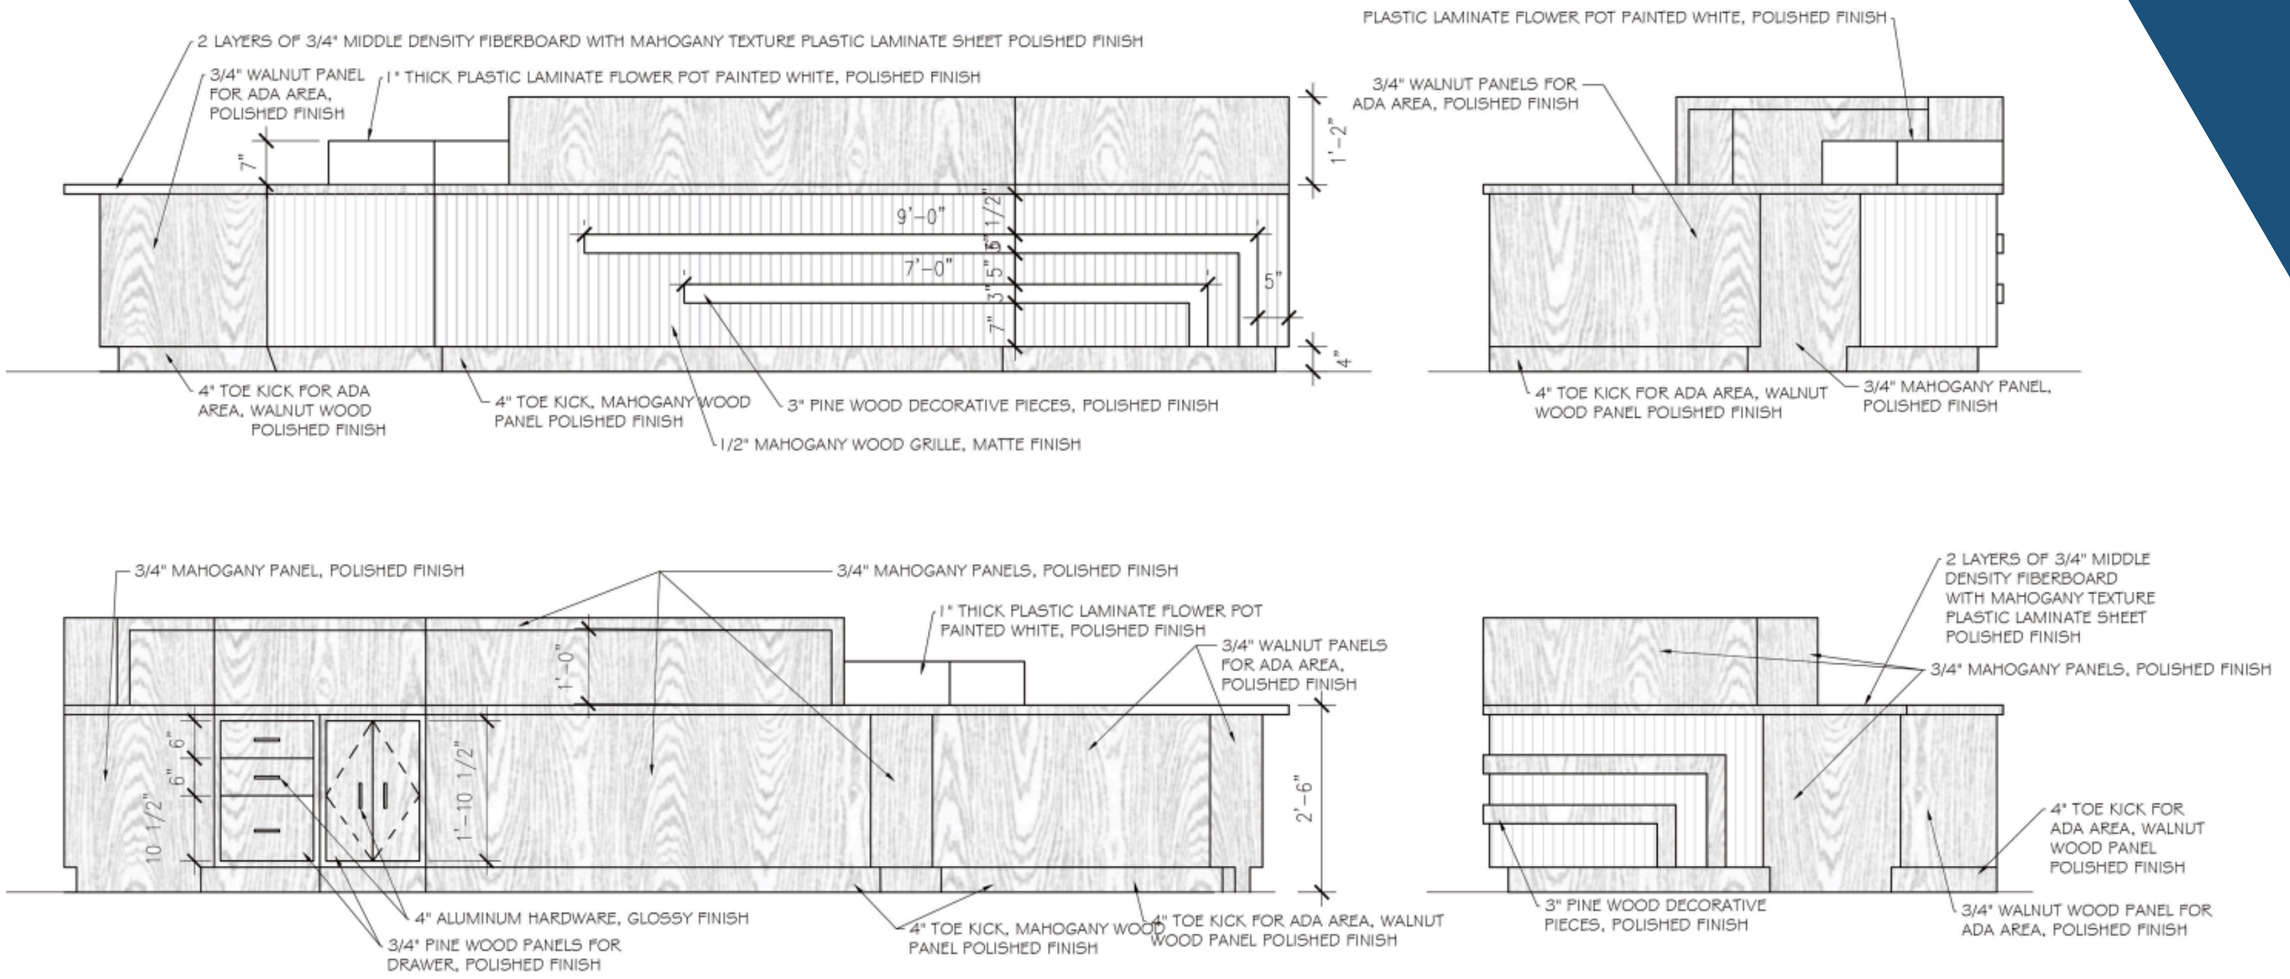

2 LAYERS OF 3/4" MIDDLE DENSITY FIBERBOARD WITH MAHOGANY TEXTURE PLASTIC LAMINATE SHEET POLISHED FINISH
3/4" WALNUT PANEL FOR ADA AREA, POLISHED FINISH
1" THICK PLASTIC LAMINATE FLOWER POT PAINTED WHITE, POLISHED FINISH
7"
9'-0"
7'-0"
6 1/2"
5"
3"
7"
1'-2"
5"
4"
4" TOE KICK FOR ADA AREA, WALNUT WOOD POLISHED FINISH
4" TOE KICK, MAHOGANY WOOD PANEL POLISHED FINISH
3" PINE WOOD DECORATIVE PIECES, POLISHED FINISH
1/2" MAHOGANY WOOD GRILLE, MATTE FINISH
PLASTIC LAMINATE FLOWER POT PAINTED WHITE, POLISHED FINISH
3/4" WALNUT PANELS FOR ADA AREA, POLISHED FINISH
4" TOE KICK FOR ADA AREA, WALNUT WOOD PANEL POLISHED FINISH
3/4" MAHOGANY PANEL, POLISHED FINISH
3/4" MAHOGANY PANEL, POLISHED FINISH
3/4" MAHOGANY PANELS, POLISHED FINISH
1" THICK PLASTIC LAMINATE FLOWER POT PAINTED WHITE, POLISHED FINISH
3/4" WALNUT PANELS FOR ADA AREA, POLISHED FINISH
1'-0"
6"
6"
10 1/2"
1'-10 1/2"
2'-6"
4" ALUMINUM HARDWARE, GLOSSY FINISH
3/4" PINE WOOD PANELS FOR DRAWER, POLISHED FINISH
4" TOE KICK, MAHOGANY WOOD PANEL POLISHED FINISH
4" TOE KICK FOR ADA AREA, WALNUT WOOD PANEL POLISHED FINISH
2 LAYERS OF 3/4" MIDDLE DENSITY FIBERBOARD WITH MAHOGANY TEXTURE PLASTIC LAMINATE SHEET POLISHED FINISH
3/4" MAHOGANY PANELS, POLISHED FINISH
4" TOE KICK FOR ADA AREA, WALNUT WOOD PANEL POLISHED FINISH
3" PINE WOOD DECORATIVE PIECES, POLISHED FINISH
3/4" WALNUT WOOD PANEL FOR ADA AREA, POLISHED FINISH


ELEVATIONS

SECTIONS

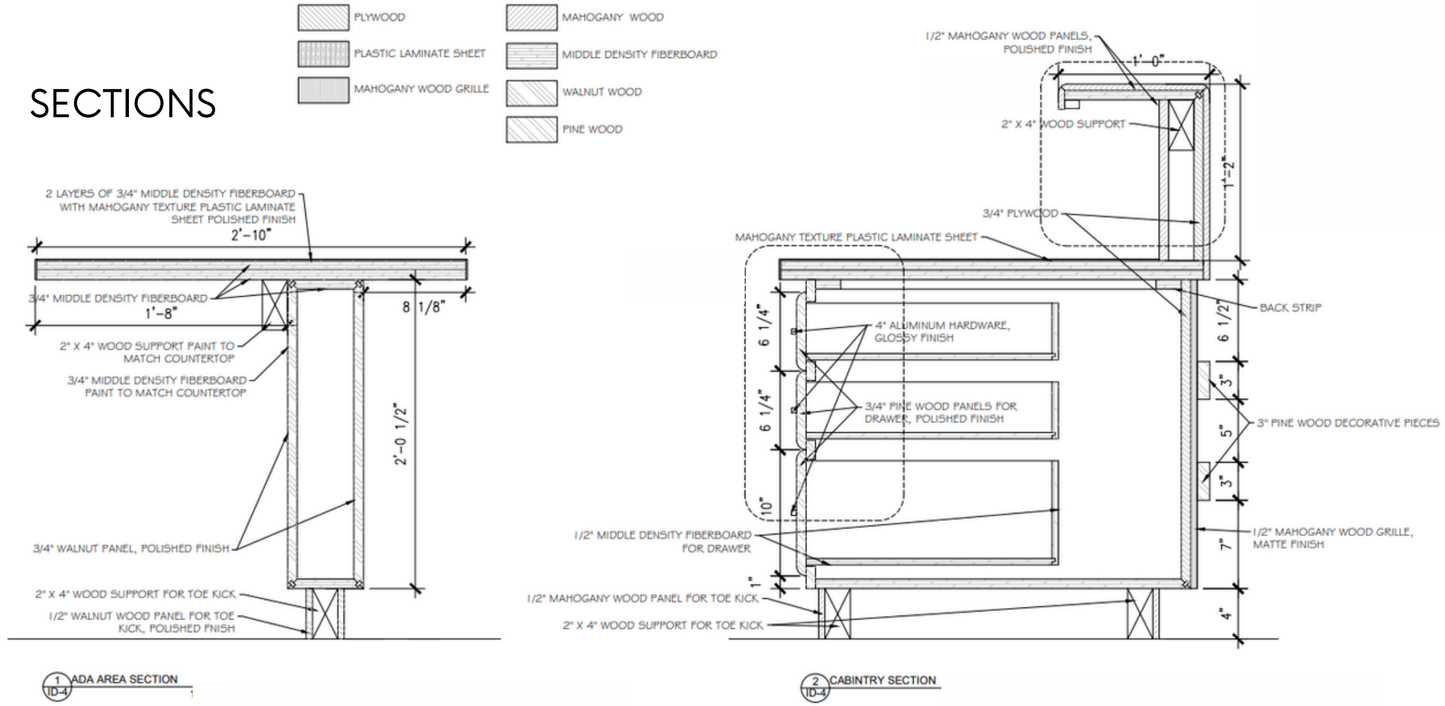

DETAILS

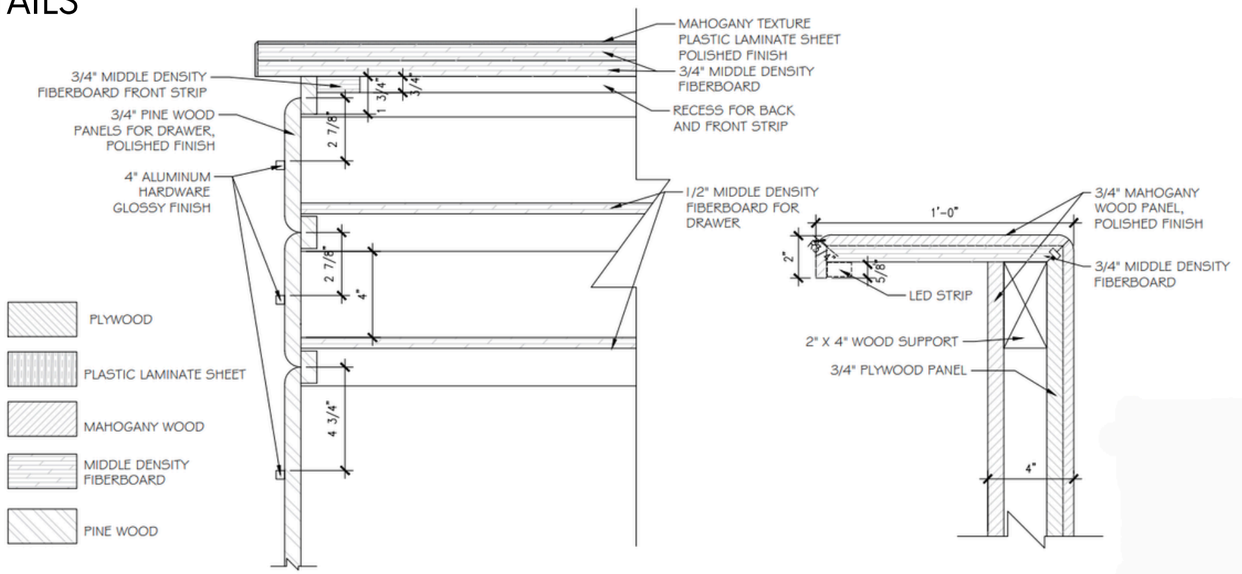

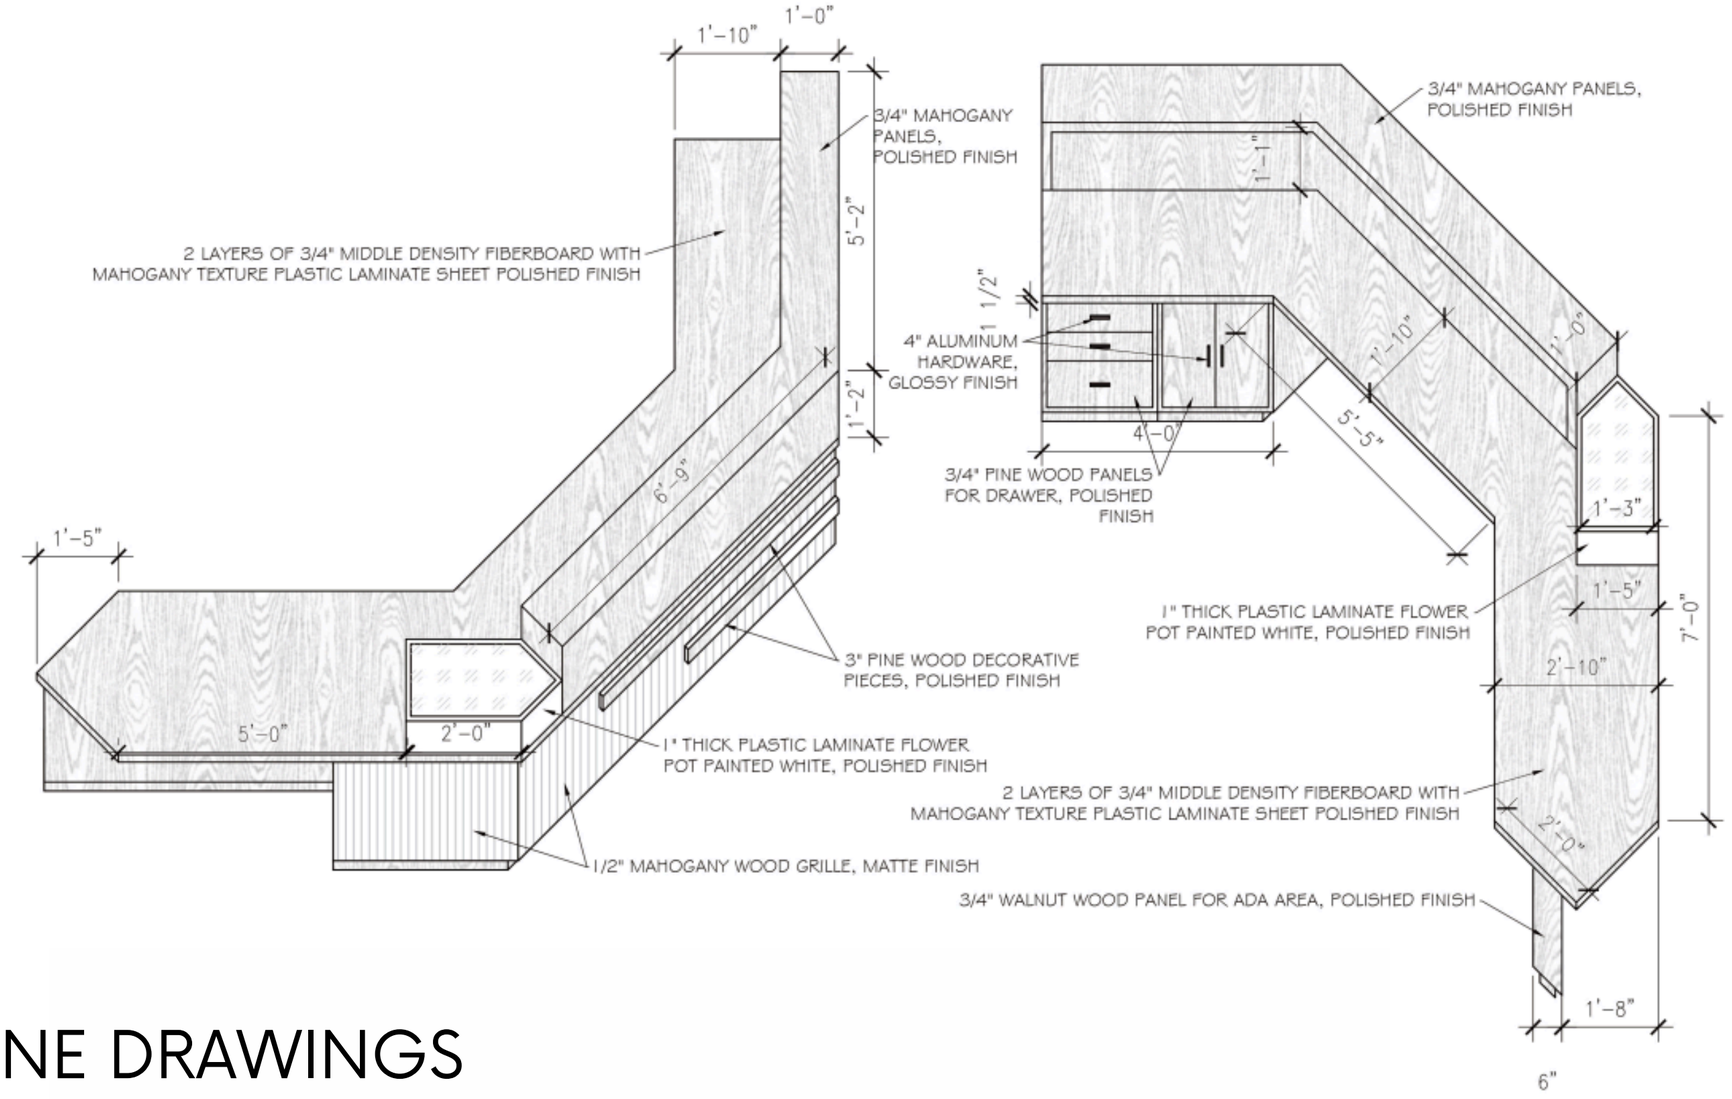

PARALINE DRAWINGS